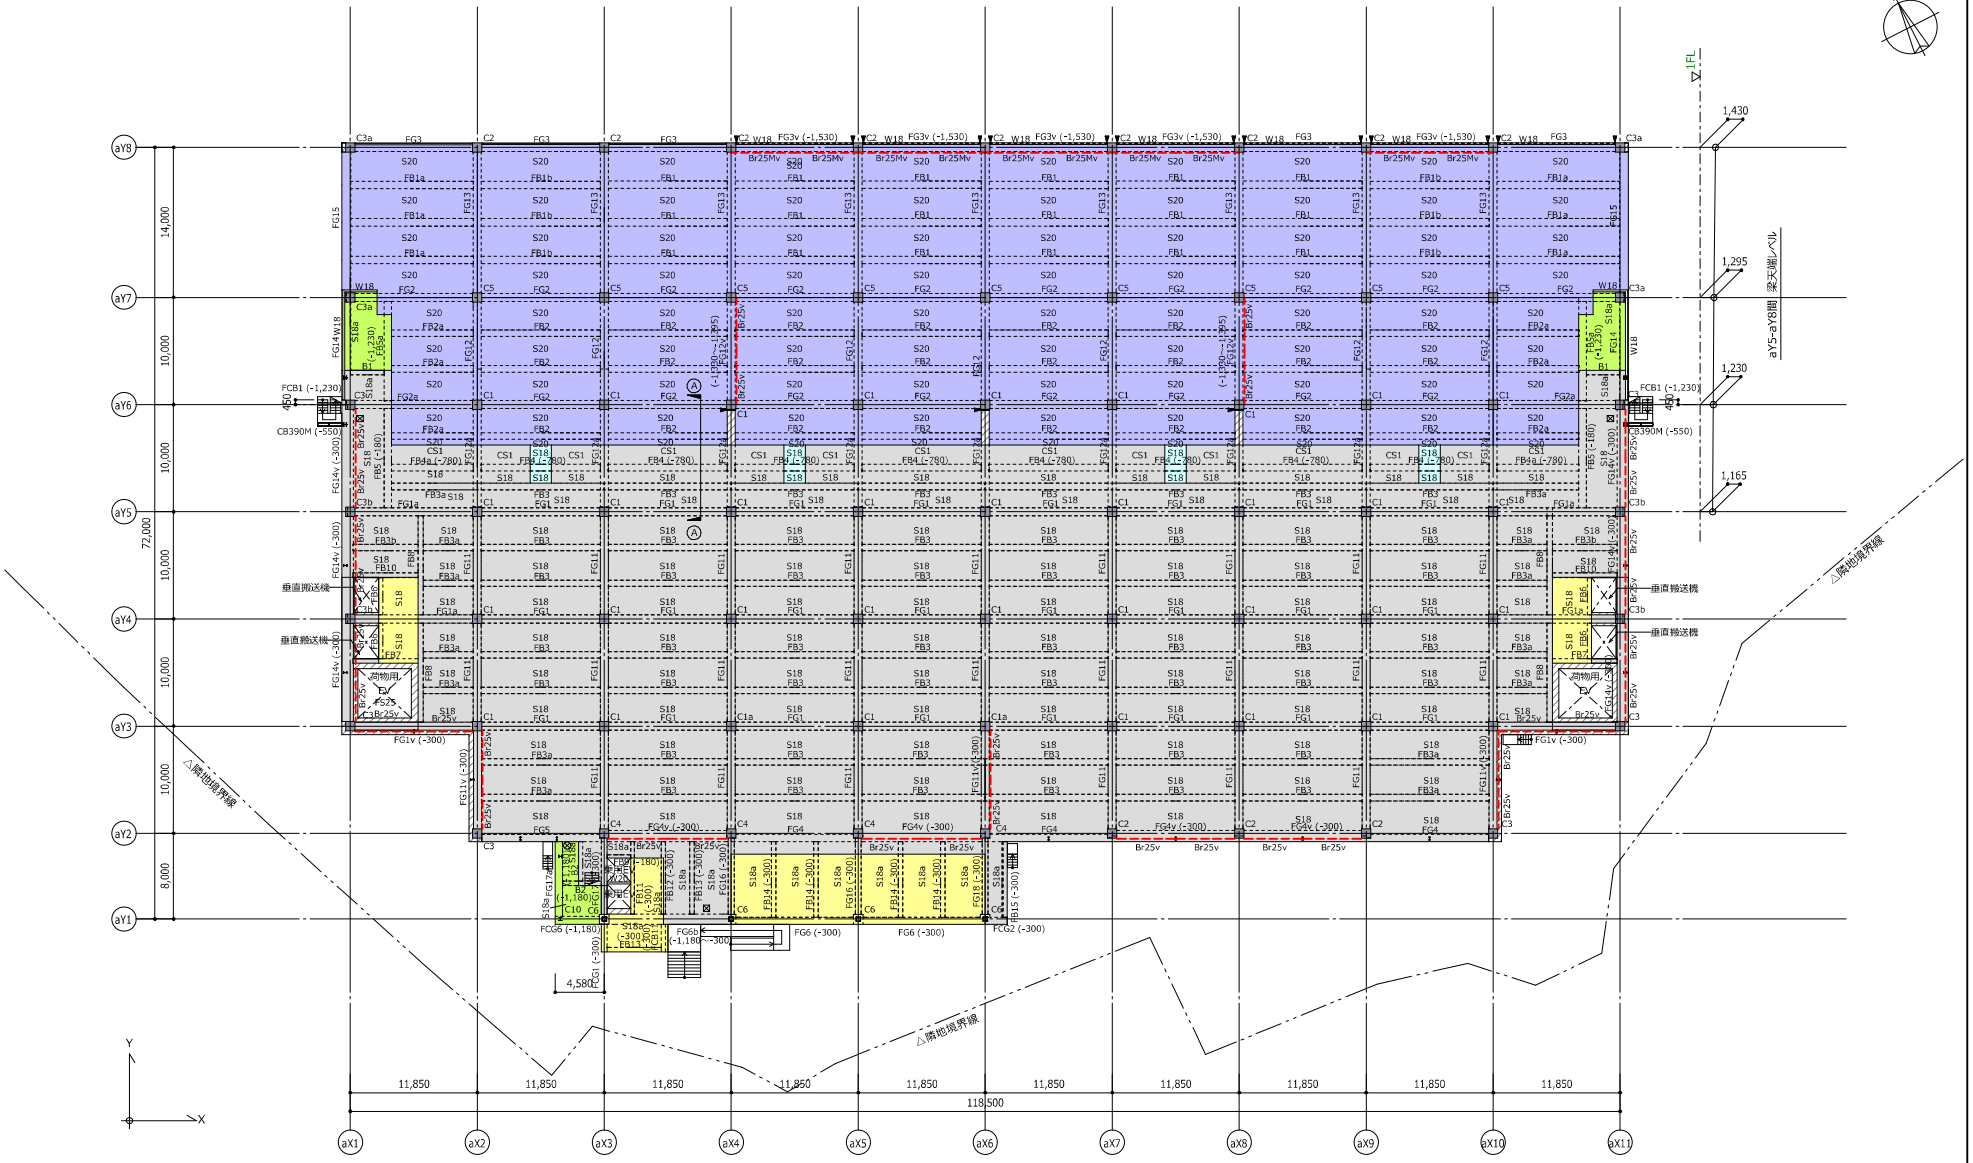

1階伏図　1：500

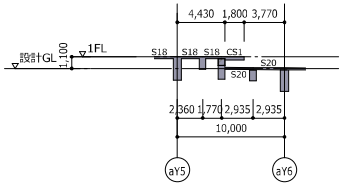

A-A断面図　1：500

特記なき限り下記による。

1.スラブ、梁天端レベルは、別表による。
2.（　）内は、FLからの梁天端レベルを示す。
3.スラブの主筋方向は、符号の向きで示す。
S 主筋方向　U 主筋方向
4. ⊗ は、マンホールを示す。
5. ⊠ は、点検口を示す。
6. ▨ は、増しコン範囲を示す。
7.CS1下部のスラブはS20とする。
スラブ天端レベルは水勾配による。(A-A断面図参照)

8.▼は、鉛直躯体スリットを示す。
エラスタイト等で縁切りを行うこと。
スリット幅は、15mmとする。

凡例	スラブ天端	大梁天端	小梁天端	備　考
	FL±0	FL-180	FL-180	
	水勾配による	水勾配-200	水勾配-200	
	FL-100	FL-180	FL-180	事務所、垂直搬送機
	FL-600	-	-	
	FL-1,000	FL-1,180	FL-1,180	
	FL-1,090	-	-	

株式会社フジタ

一級建築士事務所

工事名称
（仮称）厚木市森の里
物流施設新築工事

設計番号　00-23-1075

実行部署の長
三輪　若菜

設計担当者
一級 第365397号
加奈森　聡

一級 第384948号
上村　直人

法適合確認結果等
構造設計一級建築士
第8730号
三輪　若菜
構造関係規定に適合することを確認した。

注記

【実施設計図】

年月日　2024.12.02

図面名称
1階伏図

S 0403

Revit

Copyright (C) 株式会社フジタ 著作権者の許可なく複製、転載、第三者開示等の行為を禁止する。

2階伏図　　1：500

特記なき限り下記による。

1.スラブ、梁天端レベルは、別表による。
2.（　）内は、FLからの梁天端レベルを示す。
3. ⊕ は、剛接合を示す。
4.スラブの主筋方向は、符号の向きで示す。
S 主筋方向　U 主筋方向
5. ═══ は、横補剛材b2を示す。
6. ▽ は、COV.PL補強を示す。
7.水平ブレースはHBr20Mとする。

凡例	スラブ天端	大梁天端	小梁天端	備　考
	FL±0	FL-180	FL-180	
	FL-100	FL-380	FL-280	事務所、垂直搬送機

株式会社フジタ

一級建築士事務所

工事名称
（仮称）厚木市森の里
物流施設新築工事

設計番号　00-23-1075

実行部署の長
三輪　若菜

設計担当者
一級 第365397号
加奈森　聡

一級 第384948号
上村　直人

法適合確認結果等
構造設計一級建築士
第8730号
三輪　若菜
構造関係規定に適合することを確認した。

注記

【実施設計図】

年月日　2024.12.02

図面名称
2階伏図

S 0404

Revit

Copyright (C) 株式会社フジタ　著作権者の許可なく複製、転載、第三者開示等の行為を禁止する。

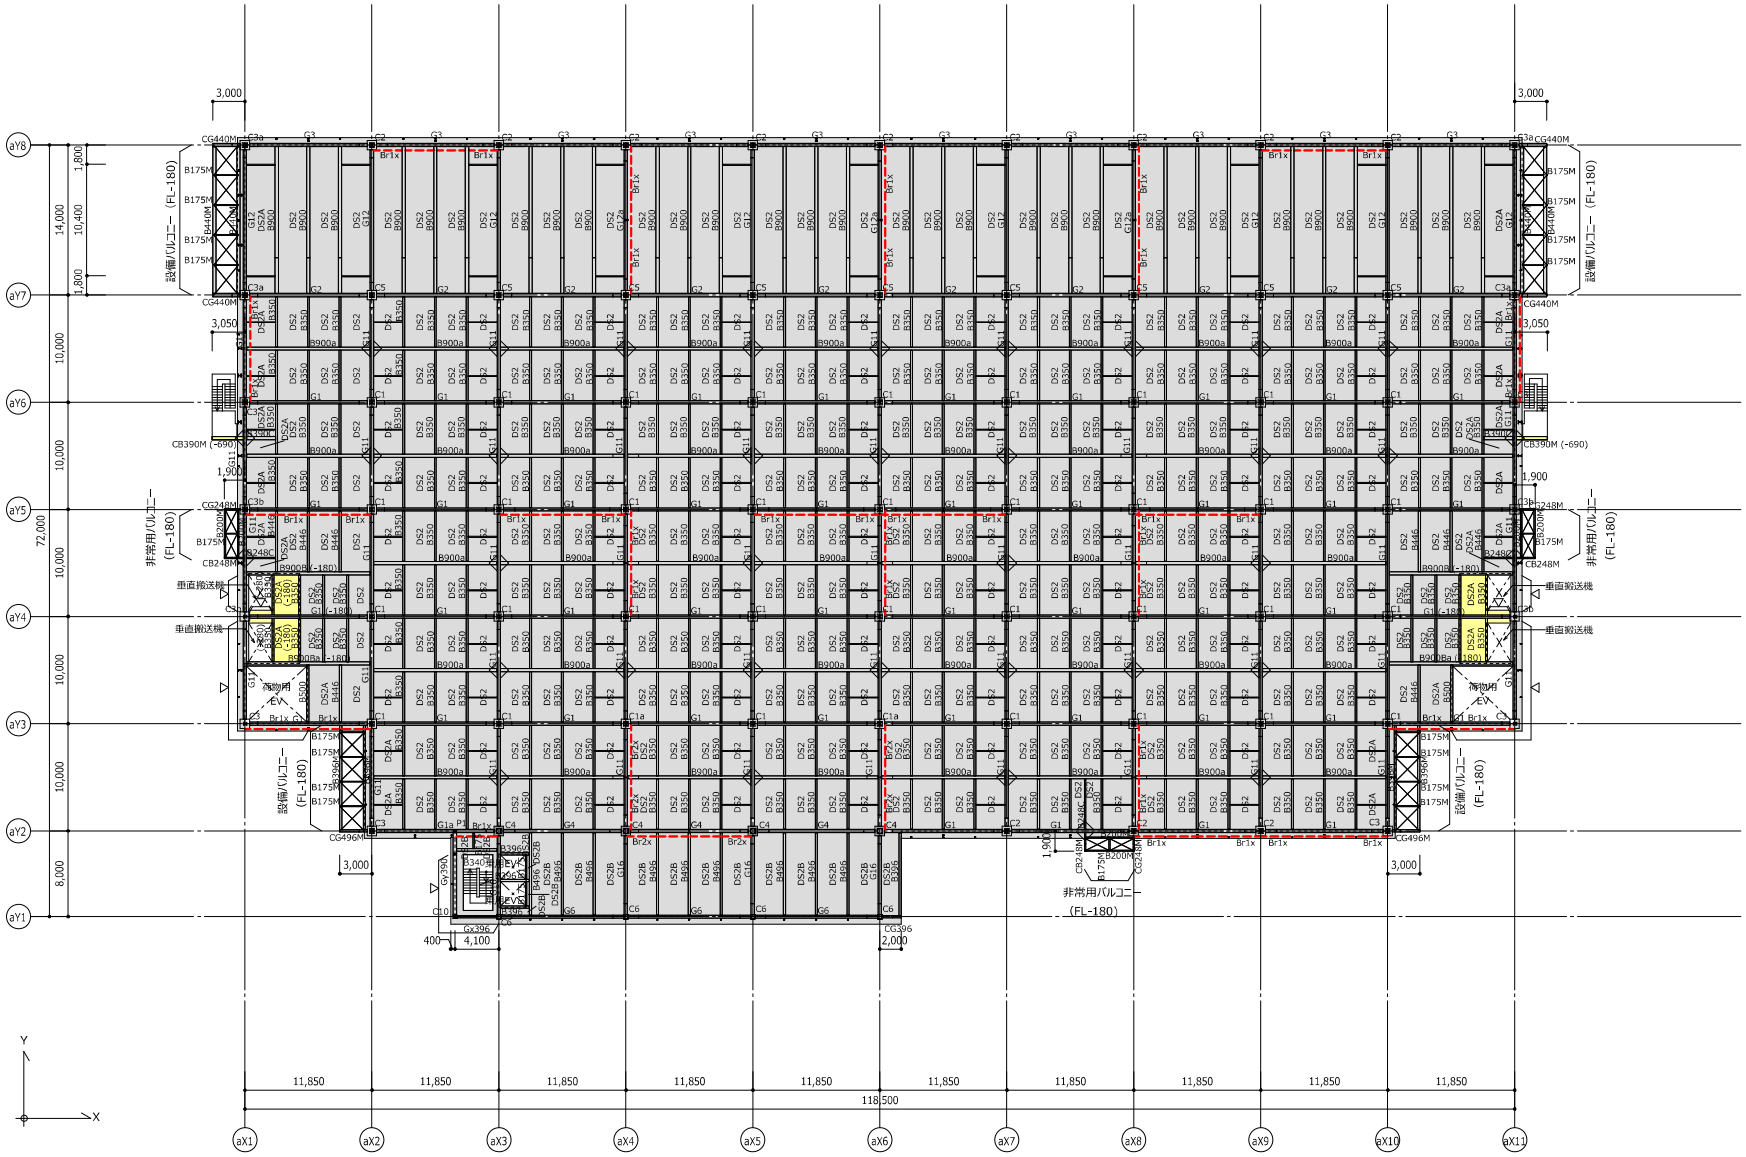

3階伏図　　1：500

特記なき限り下記による。

1.スラブ、梁天端レベルは、別表による。
2.（　）内は、FLからの梁天端レベルを示す。
3. ⊕ は、剛接合を示す。
4.スラブの主筋方向は、符号の向きで示す。
S 主筋方向　U 主筋方向
5. ═══ は、横補剛材b2を示す。
6. ▽ は、COV.PL補強を示す。
7.水平ブレースはHBr20Mとする。

凡例	スラブ天端	大梁天端	小梁天端	備　考
	FL±0	FL-180	FL-180	
	FL-100	FL-380	FL-280	事務所、垂直搬送機

株式会社フジタ

一級建築士事務所

工事名称
（仮称）厚木市森の里
物流施設新築工事

設計番号　00-23-1075

実行部署の長
三輪　若菜

設計担当者
一級 第365397号
加奈森　聡

一級 第384948号
上村　直人

法適合確認結果等
構造設計一級建築士
第8730号
三輪　若菜
構造関係規定に適合することを確認した。

注記

【実施設計図】

年月日　2024.12.02

図面名称
3階伏図

S 0405

Copyright (C) 株式会社フジタ　著作権者の許可なく複製、転載、第三者開示等の行為を禁止する。

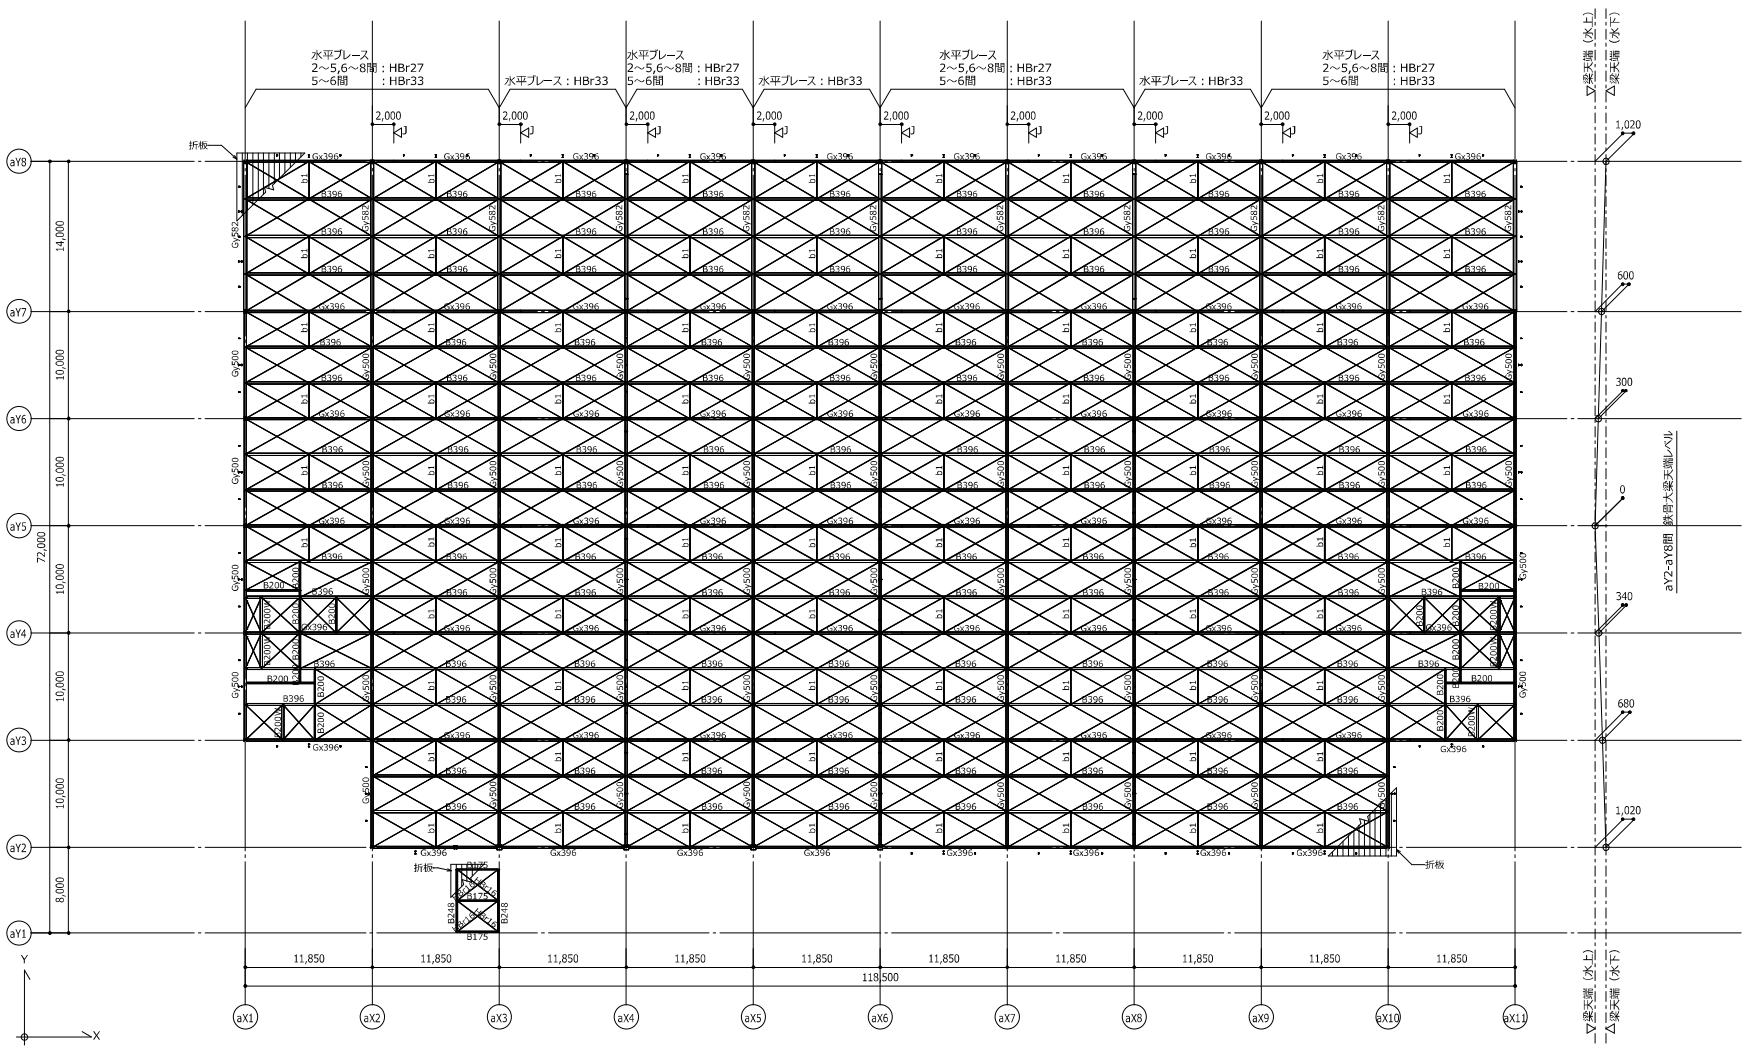

屋根伏図　1：500

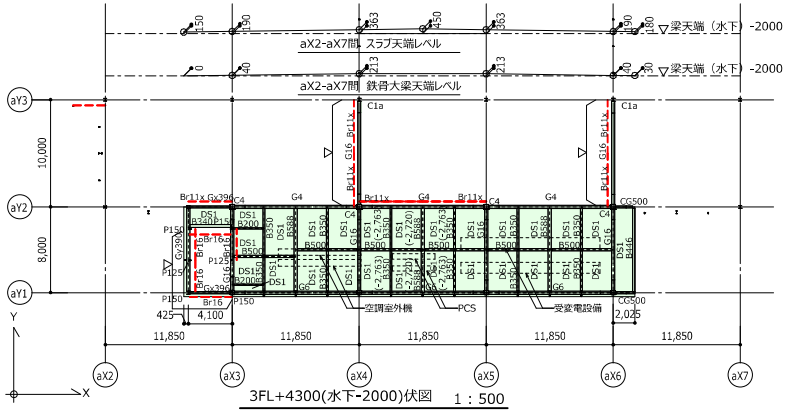

3FL+4300(水下-2000)伏図　1：500

凡例	スラブ天端	大梁天端	小梁天端	備　考
	–	水勾配による	水勾配による	
	水勾配による	水勾配による	水勾配による	

特記なき限り下記による。

1.屋根勾配は意匠図参照。

2.の梁天端レベルは水勾配による。

3.▽は、COV.PL補強を示す。

株式会社フジタ

一級建築士事務所

工事名称

（仮称）厚木市森の里
物流施設新築工事

設計番号　00-23-1075

実行部署の長

三輪　若菜

設計担当者

一級 第365397号
加奈森　聡

一級 第384948号
上村　直人

法適合確認結果等
構造設計一級建築士
第8730号
三輪　若菜
構造関係規定に適合することを
確認した。

注記

【実施設計図】

年月日　2024.12.02

図面名称

R階伏図

S 0406

Revit

Copyright (C) 株式会社フジタ 著作権者の許可なく複製、転載、第三者開示等の行為を禁止する。

鉄骨大梁断面表

特記なき限り下記による。

1.始端・中央・終端部材の範囲は下図による。

大梁の取りつく通り名の数字の小さい方を「始端」、数字の大きい方を「終端」とする。

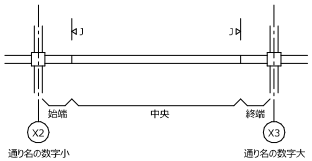

2.HY材は断面性能が同等のBH材への置換えを可とする。

COV.PL補強要領図

特記なき限り下記による。

1.溶接記号○○○-○○○は溶接長さ-間隔を示す。

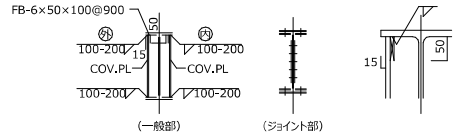

(FB取付要領)

・溶接による歪みが生じない様に留意し、必要に応じて対策を講じること。

符号	部材断面	材質	COV.PL	備考
RG16	H-488x300x11x18	SM490A	PL-9	
3G1	H-700x300x13x24	SM490A	PL-9	
3G11	H-900x300x16x28	SM490A	PL-9	
2G1	H-700x300x13x24	SM490A	PL-9	
2G11	H-900x300x16x28	SM490A	PL-9	
Gy390	H-390x300x10x16	SS400	PL-6	
Gx396	H-396x199x 7x11	SS400	PL-6	

符号	階	始端		中央		終端		備考
		材質	部材	材質	部材	材質	部材	
G1	3階	SM490A	H-700x300x13x24	SM490A	H-700x300x13x24	SM490A	H-700x300x13x24	
G1	2階	SM490A	H-700x300x13x24	SM490A	H-700x300x13x24	SM490A	H-700x300x13x24	
G1a	3階	SM490A	H-700x300x14x28	SM490A	H-700x300x14x28	SM490A	H-700x300x14x28	外法一定材
G2	3階	SM490A	H-900x300x19x32	SM490A	H-900x300x19x32	SM490A	H-900x300x19x32	外法一定材
G2	2階	SM490A	H-900x300x19x32	SM490A	H-900x300x19x32	SM490A	H-900x300x19x32	外法一定材
G3	3階	SM490A	H-900x300x16x28	SM490A	H-900x300x16x28	SM490A	H-900x300x16x28	
G3	2階	SM490A	H-900x300x16x28	SM490A	H-900x300x16x28	SM490A	H-900x300x16x28	
G4	R階	SM490A	H-692x300x13x20	SM490A	H-692x300x13x20	SM490A	H-692x300x13x20	
G4	3階	SM490A	H-700x300x13x24	SM490A	H-700x300x13x24	SM490A	H-700x300x13x24	
G4	2階	SM490A	H-700x300x13x24	SM490A	H-700x300x13x24	SM490A	H-700x300x13x24	
G6	R階	SM490A	H-692x300x13x20	SM490A	H-692x300x13x20	SM490A	H-692x300x13x20	
G6	3階	SM490A	H-488x300x11x18	SM490A	H-488x300x11x18	SM490A	H-488x300x11x18	
G6	2階	SM490A	H-488x300x11x18	SM490A	H-488x300x11x18	SM490A	H-488x300x11x18	
G11	3階	SM490A	H-900x300x16x28	SM490A	H-900x300x16x28	SM490A	H-900x300x16x28	
G11	2階	SM490A	H-900x300x16x28	SM490A	H-900x300x16x28	SM490A	H-900x300x16x28	
G12	3階	SM490A	H-900x300x16x28	SM490A	H-900x300x16x28	SM490A	H-900x300x16x28	
G12	2階	SM490A	H-900x300x16x28	SM490A	H-900x300x16x28	SM490A	H-900x300x16x28	
G12a	3階	SM490A	H-900x300x16x28	SM490A	H-900x300x16x28	SM490A	H-900x300x16x28	
G12a	2階	SM490A	H-900x300x16x28	SM490A	H-900x300x16x28	SM490A	H-900x300x16x28	
G16	R階	SM490A	H-488x300x11x18	SM490A	H-488x300x11x18	SM490A	H-488x300x11x18	
G16	3階	SM490A	H-488x300x11x18	SM490A	H-488x300x11x18	SM490A	H-488x300x11x18	
G16	2階	SM490A	H-488x300x11x18	SM490A	H-488x300x11x18	SM490A	H-488x300x11x18	
Gx396	R階	SS400	H-396x199x7x11	SS400	H-396x199x7x11	SS400	H-396x199x7x11	H-441x199x6x9.5へ置換え可　ピン接合
Gx396	3階	SS400	H-396x199x7x11	SS400	H-396x199x7x11	SS400	H-396x199x7x11	H-441x199x6x9.5へ置換え可　ピン接合
Gx396	2階	SS400	H-396x199x7x11	SS400	H-396x199x7x11	SS400	H-396x199x7x11	H-441x199x6x9.5へ置換え可　ピン接合
Gy390	R階	SS400	H-390x300x10x16	SS400	H-390x300x10x16	SS400	H-390x300x10x16	ピン接合
Gy390	3階	SS400	H-390x300x10x16	SS400	H-390x300x10x16	SS400	H-390x300x10x16	ピン接合
Gy390	2階	SS400	H-390x300x10x16	SS400	H-390x300x10x16	SS400	H-390x300x10x16	ピン接合
Gy500	R階	SS400	H-500x200x10x16	SS400	H-500x200x10x16	SS400	H-500x200x10x16	ピン接合
Gy582	R階	SS400	H-582x300x12x17	SS400	H-582x300x12x17	SS400	H-582x300x12x17	ピン接合

株式会社フジタ

一級建築士事務所

工事名称

（仮称）厚木市森の里
物流施設新築工事

設計番号　00-23-1075

実行部署の長

三輪　若菜

設計担当者

一級 第365397号
加奈森　聡

一級 第384948号
上村　直人

法適合確認結果等
構造設計一級建築士
第8730号
三輪　若菜
構造関係規定に適合することを
確認した。

注記

【実施設計図】

年月日　2024.12.02

図面名称

鉄骨大梁断面表

S 0616

Revit

Copyright (C) 株式会社フジタ　著作権者の許可なく複製、転載、第三者開示等の行為を禁止する。